


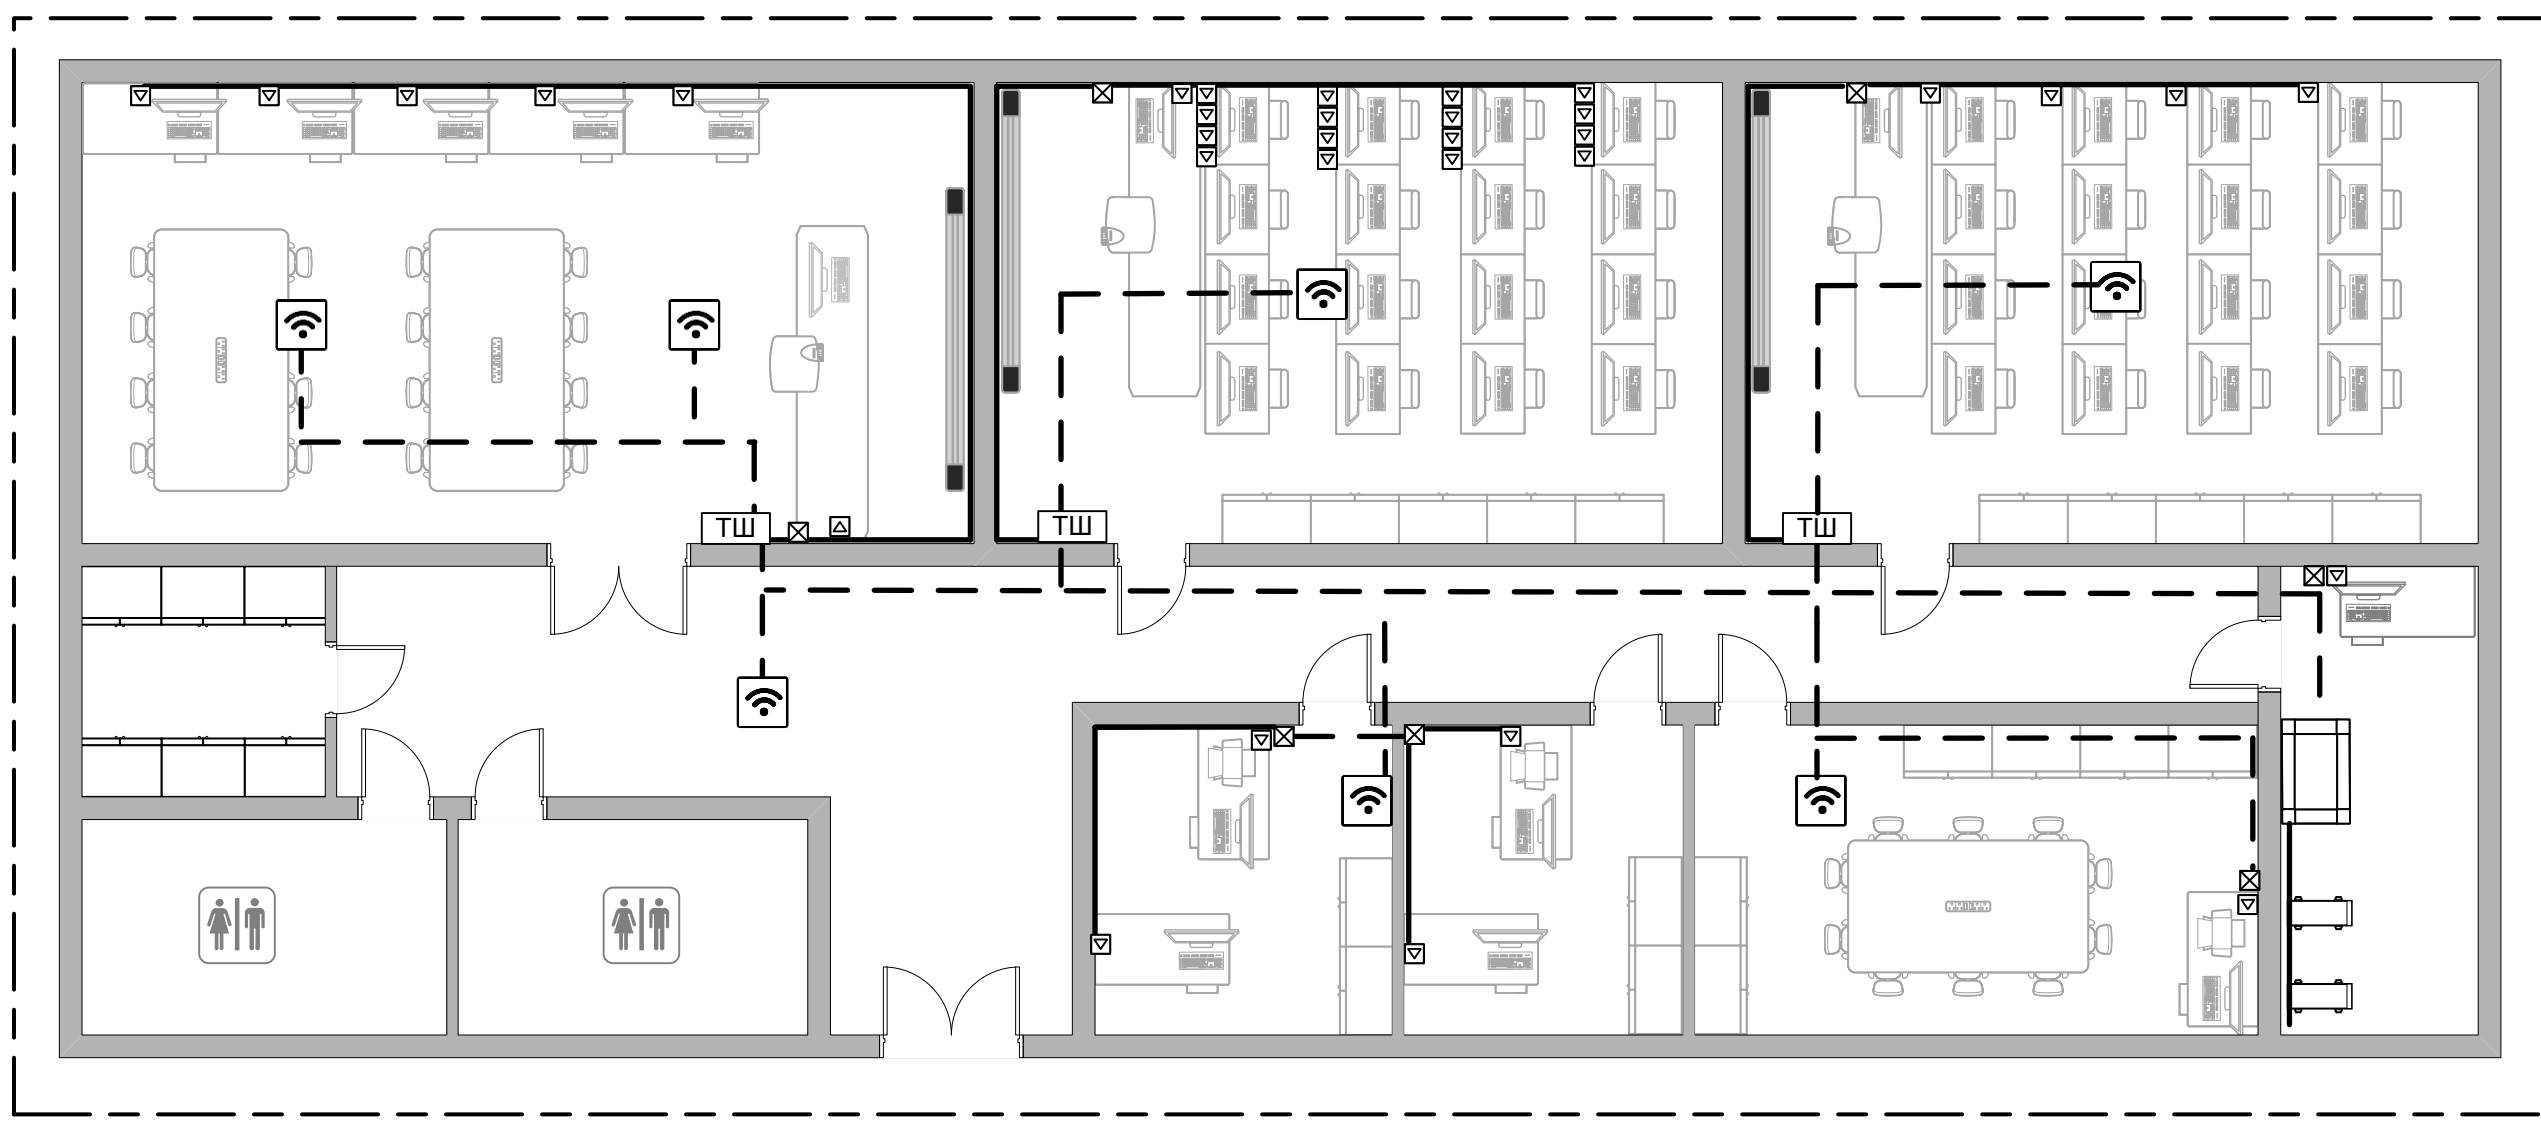

Технические рекомендации

Кабель везде прокладывается в кабель-канале вдоль стены на расстоянии 30 см от потолка.
Информационные розетки располагаются на высоте 50 см от пола, в данных местах кабель опускается вертикально вниз.
Телекоммуникационный шкаф крепится на расстоянии 150 см от пола.
Беспроводные точки доступа монтируются к фальш-потолку.

Условные обозначения

- | | | | |
|--|---|--|------------------------------------|
| | Пользовательская станция | | Железобетонная стена |
| | Проекторная доска МФУ | | Газосиликатная стена |
| | Проектор | | Точка доступа |
| | Сервер (Ф - файловый, 3 – загрузки ОС) | | Прокладка кабеля в коробе |
| | Стойка настенная | | Кабель в коробе над фальш-потолком |
| | Телекоммуникационный шкаф навесной с коммутатором | | Тип короба/кол-во кабеля в коробе |

ГЧИР.400201.205 СЗ

					ГЧИР.400201.205 СЗ				
					Локальная компьютерная сеть. План этажа	Лит.	Масса	Масштаб	
Изм.	Лист	№ докум.	Подп.	Дата					
Разраб.	Бригадир					Т			
Пров.	Глецевич								
Т. контр.						Лист	Листов	1	
Реценз.						ЭВМ, гр. 250502			
Н. контр.									
Утв.									