


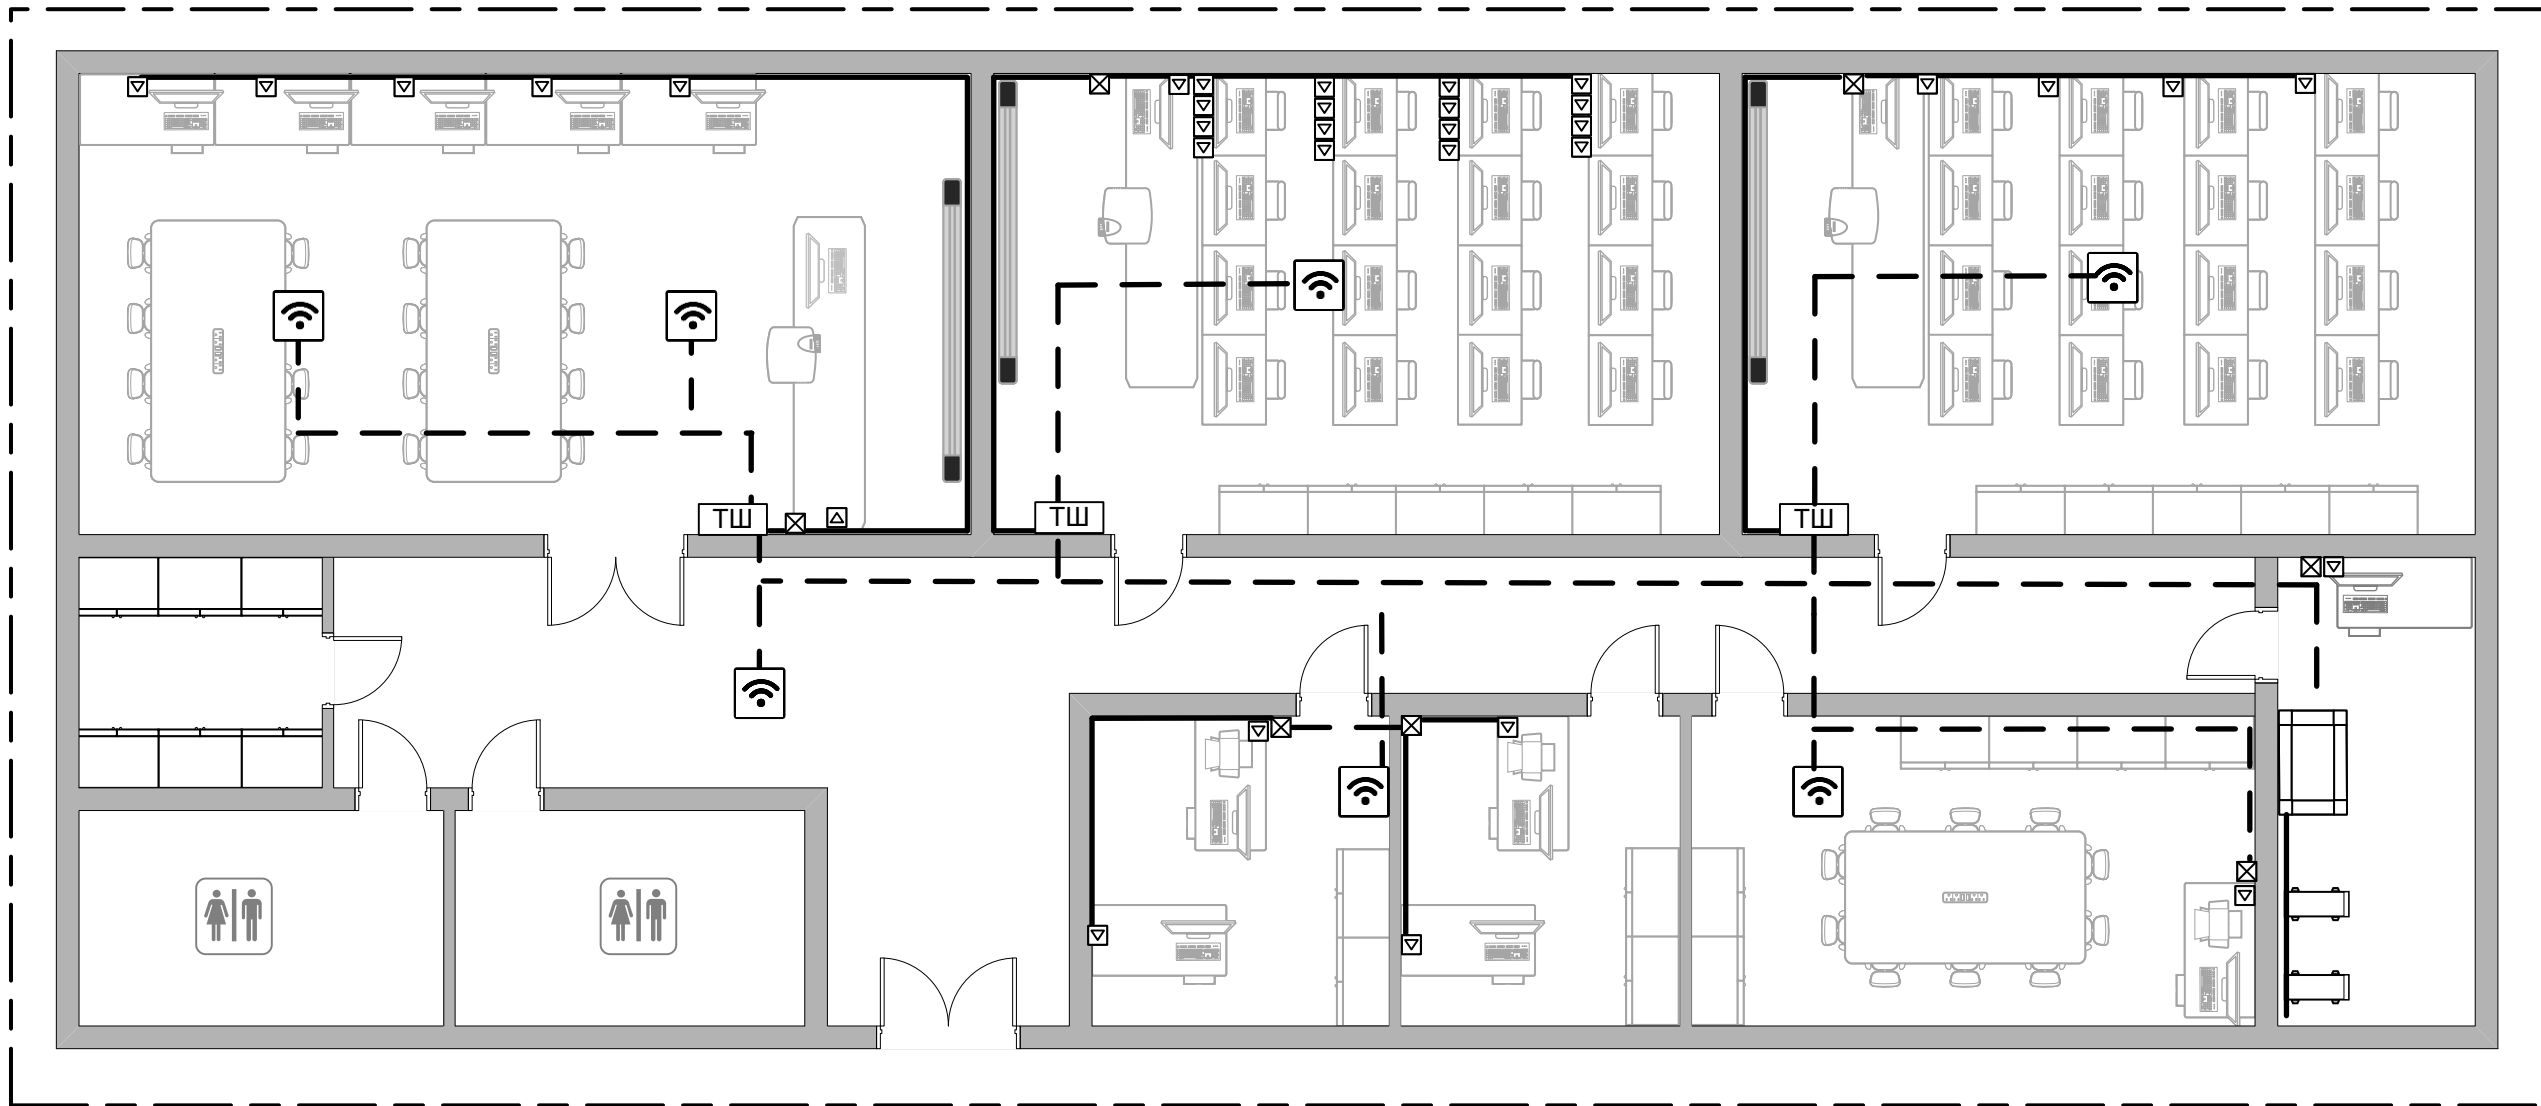

Условные обозначения					
	Пользовательская станция		Железобетонная стена		Прокладка кабеля в коробе
	Проекторная доска		Газосиликатная стена		Кабель в коробе над фальш-потолком
	МФУ		Точка доступа		XXXXXX Тип короба/кол-во кабеля в коробе
	Проектор		Стойка настенная		
	Сервер (Ф - файловый, 3 – загрузки ОС)		ТШ Телекоммуникационный шкаф навесной с коммутатором		

					ГЧИР.400201.205 СЗ				
					Локальная компьютерная сеть. План этажа	Лит.		Масса	Масштаб
							Т		
						Лист		Листов 1	
						ЭВМ, гр. 250502			
Изм.	Лист	№ докум.	Подп.	Дата					
Разраб.	Бригадир								
Пров.	Глецевич								
Т. контр.									
Реценз.									
Н. контр.									
Утв.									